NORTH ELEVATION — CLADDING TAKEOFF MARKUP

SAMPLE ONLY: fictitious 1-storey commercial building, Alberta. Not from any real project or client. Cladding areas and flashing LF match the North column of the SharpBid sample cladding takeoff.

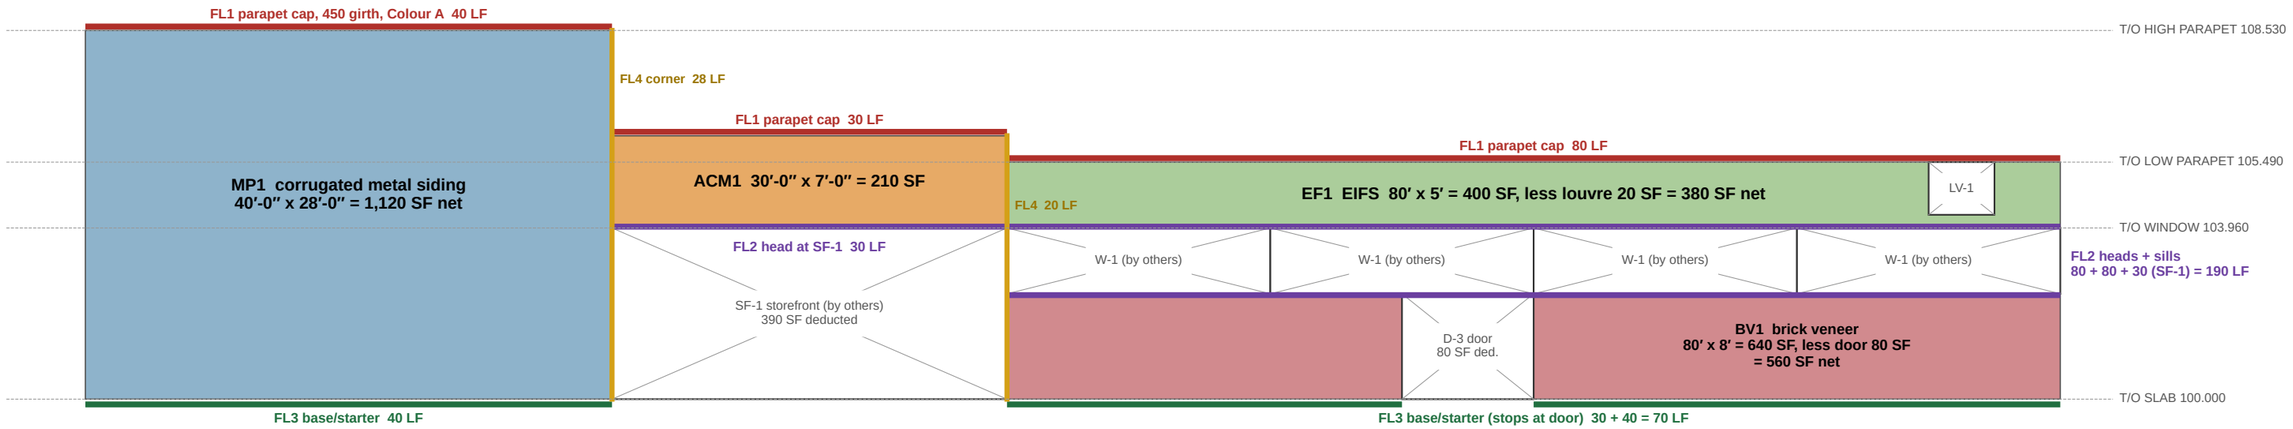

LEGEND (net of openings; openings by others hatched white with X)

	MP1	Corrugated metal siding, 0.76 mm, Colour A	EW1	**1,120 SF**
	ACM1	ACM panel, 4 mm, routed and returned, Colour B	EW2	**210 SF**
	EF1	EIFS, drainage type, 100 mm EPS	EW3	**380 SF**
	BV1	Brick veneer, modular, Colour C	EW4	**560 SF**

HOW TO READ THIS SHEET

Every coloured area is a line in the Excel takeoff, by tag, wall type and elevation.

Openings are dimensioned and deducted, so you can check each net area by hand.

Flashings and trims are drawn as coloured lines, one colour per profile; the LF shown match the workbook.

Anything unclear on the drawings goes to the questions list, not a guess.

SharpBid Estimating | sharpbid.ca | info@sharpbid.ca